


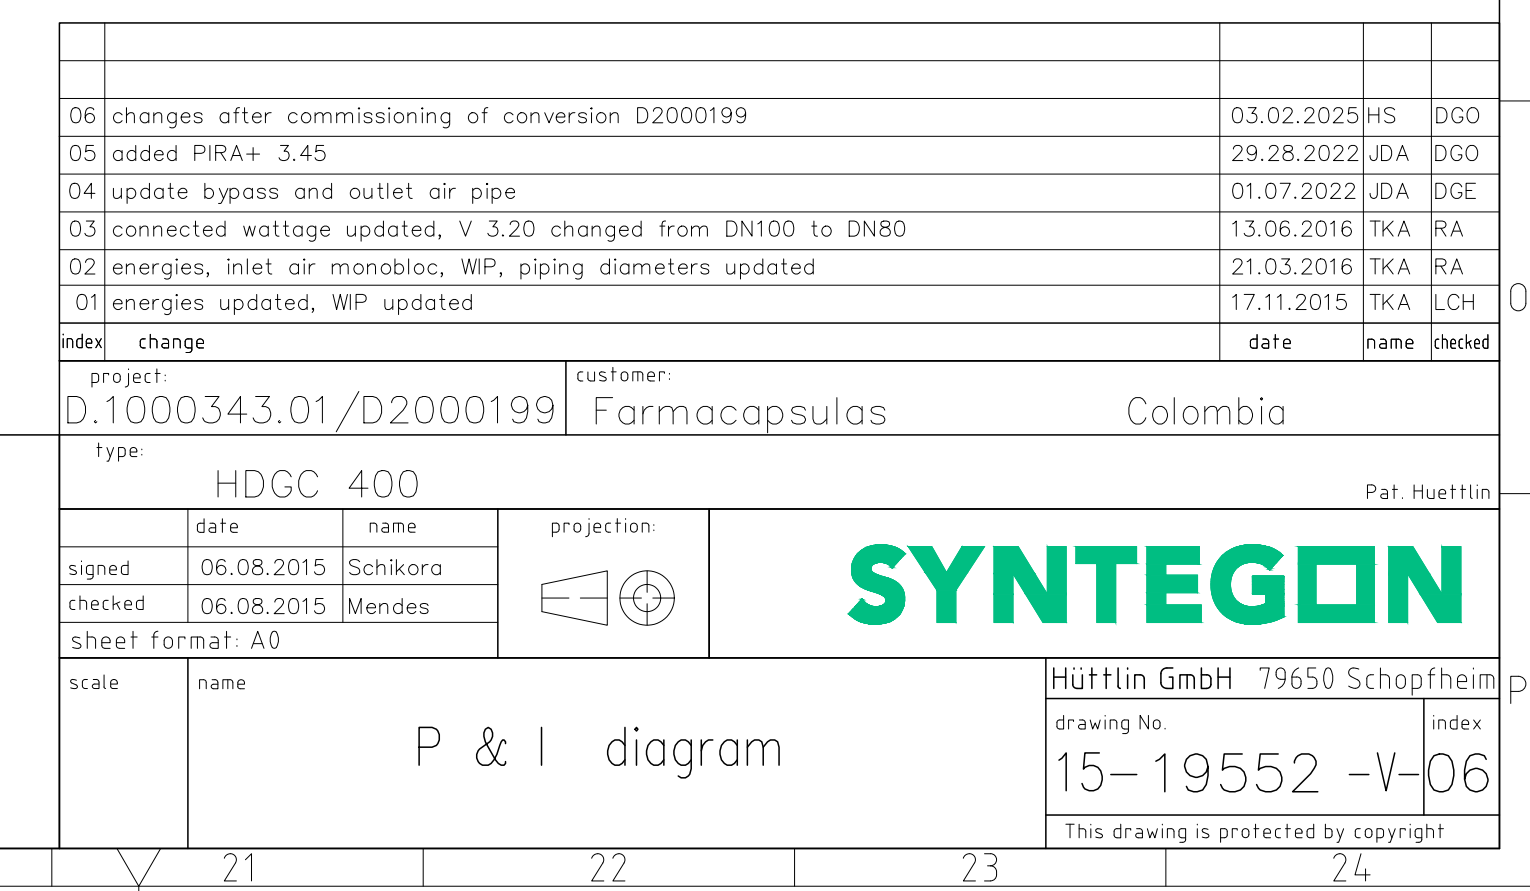

Recommended Insulation	
Fresh air to Monobloc	Armaflex, Insulation thickness = min. 19 mm
Inlet air pipe	Mineral wool with aluminium foil facing, Insulation thickness = min. 80 mm
Outlet air pipe	Mineral wool with aluminium foil facing, Insulation thickness = min. 30 mm
Transfer air pipe	Mineral wool with aluminium foil facing, Insulation thickness = min. 80 mm
W/P Pipes	Armaflex, Insulation thickness = min. 19 mm
Condensate pipes	Mineral wool with aluminium foil facing, Insulation thickness = min. 30 mm
Sleam pipes (3barli)	Mineral wool with aluminium foil facing, Insulation thickness = min. 50 mm
Condensate pipes	Mineral wool with aluminium foil facing, Insulation thickness = min. 30 mm
Cooling water 6°C-12°C	Armaflex, Insulation thickness = min. 19 mm
Hot water > 60°C	Armaflex, Insulation thickness = min. 19 mm